
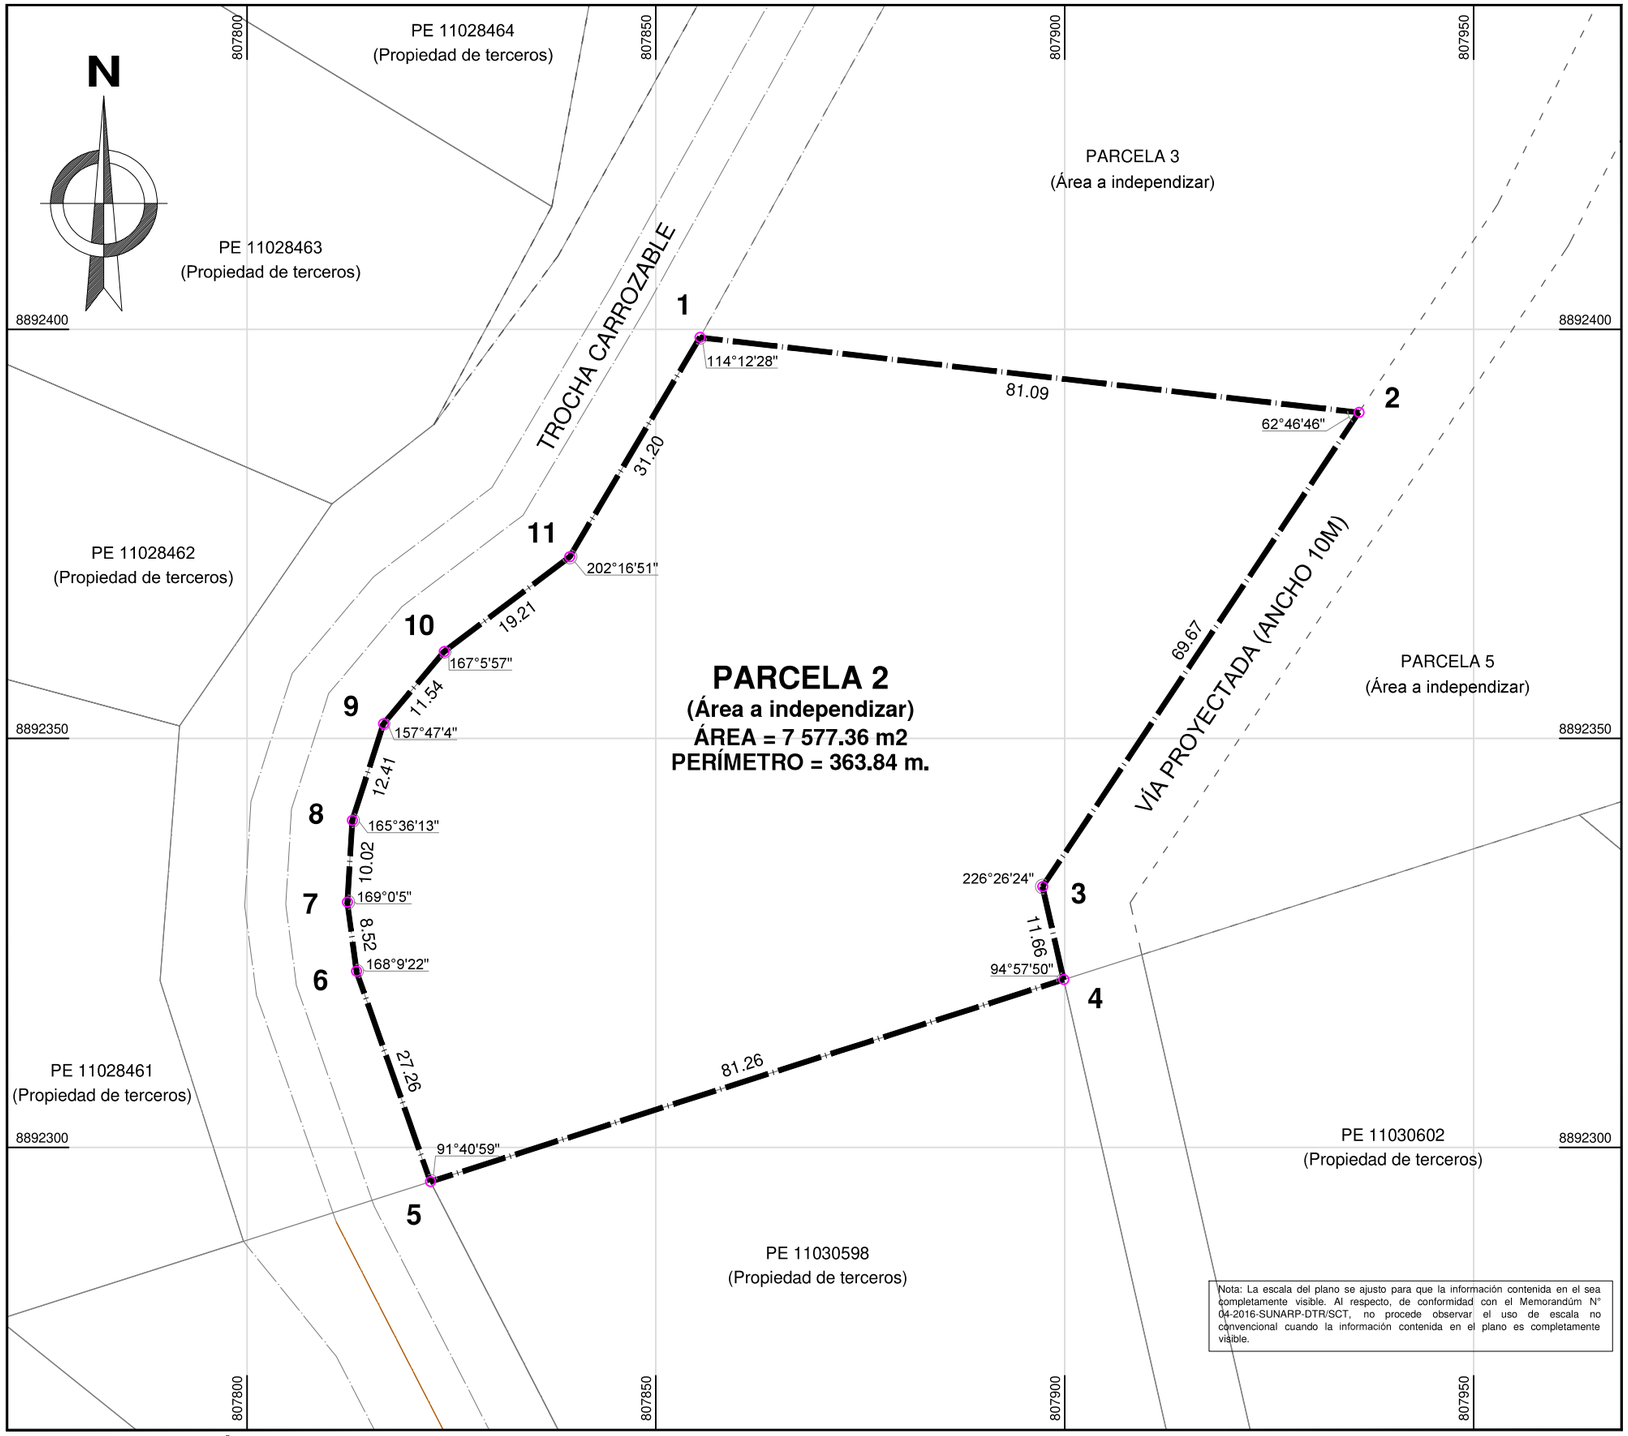


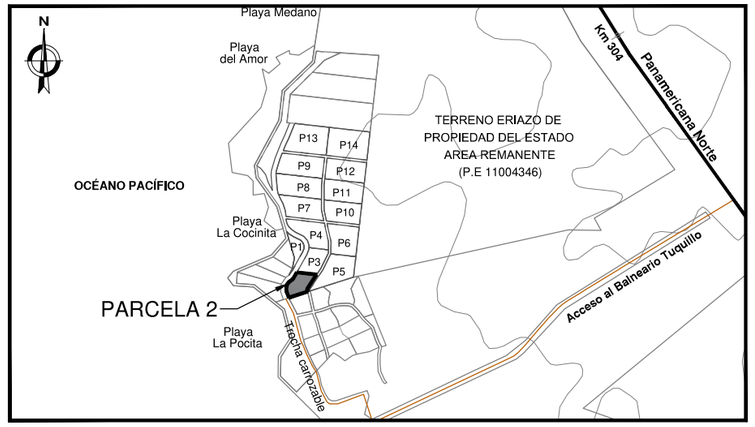

PLANO DE UBICACIÓN
ESCALA 1 / 25 000

CUADRO DE DATOS TÉCNICOS - PARCELA 2				DATUM: PSAD56, ZONA: 17S		DATUM: WGS84, ZONA: 17S	
VERTICE	LADO	DISTANCIA	ANG. INTERNO	ESTE (X)	NORTE (Y)	ESTE (X)	NORTE (Y)
1	1-2	81.09	114°12'28"	807855.3826	8892399.0175	807592.7431	8892034.1927
2	2-3	69.67	62°46'46"	807935.9514	8892389.8466	807673.3120	8892025.0217
3	3-4	11.66	226°26'24"	807897.2807	8892331.8943	807634.6413	8891967.0694
4	4-5	81.26	94°57'50"	807899.8496	8892320.5190	807637.2101	8891955.6942
5	5-6	27.26	91°40'59"	807822.4301	8892295.8270	807559.7906	8891931.0022
6	6-7	8.52	168°9'22"	807813.3879	8892321.5432	807550.7484	8891956.7184
7	7-8	10.02	169°0'5"	807812.2722	8892329.9851	807549.6327	8891965.1603
8	8-9	12.41	165°36'13"	807812.8785	8892339.9849	807550.2390	8891975.1601
9	9-10	11.54	157°47'4"	807816.6848	8892351.7933	807554.0453	8891986.9685
10	10-11	19.21	167°5'57"	807824.1160	8892360.6239	807561.4765	8891995.7990
11	11-1	31.20	202°16'51"	807839.4503	8892372.1864	807576.8108	8892007.3616
TOTAL		363.84	1619°59'59"				
Suma de ángulos (real) =			1620°00'00"				
Error acumulado =			-00°00'01"				

Nota: La escala del plano se ajusto para que la información contenida en el sea completamente visible. Al respecto, de conformidad con el Memorandúm N° 04-2016-SUNARP-DTR/SCT, no procede observar el uso de escala no convencional cuando la información contenida en el plano es completamente visible.

PLANO PERIMÉTRICO
ESCALA 1 / 750

SISTEMA DE PROYECCIÓN UTM

DÁTUM UTM PSAD56 - ZONA 17S

FUENTE : BASE GRÁFICA DE LA SBN

Esta es una copia auténtica imprimible de documento electrónico archivado en la Superintendencia Nacional de Bienes Estatales, aplicando lo dispuesto por el Art. 25 de DS.070-2013-PCM y la Tercera Disposición Complementaria Final del DS. 026-2016-PCM. Su autenticidad e integridad puede ser contrastada a través de la siguiente dirección web: http://app.sbn.gob.pe/verifica e ingresando la siguiente clave: 768B404163

Firmado digitalmente por: SOLIS CRUZADO Arquimedes FAU 20131057823 hard
Fecha: 27/05/2025 15:44:20-0500

ING. ARQUIMEDES SOLIS CRUZADO
C.I.P. 63839

SUPERINTENDENCIA NACIONAL DE BIENES ESTATALES
SUBDIRECCIÓN DE DESAROLLO INMOBILIARIO

PLANO: PLANO PERIMÉTRICO			MEMORANDUM N.°: 03046-2023/SBN-DGPE-SDDI
DENOMINACIÓN: PARCELA 2	DISTRITO: HUARMEY		CUS N.°: 99705, 99706, 99708, 99709, 99710, 99712, 99715 y 93002
	PROVINCIA: HUARMEY		ÁREA: --- ---
	DEPARTAMENTO: ANCASH		DÁTUM: PSAD56 / ZONA: 17 SUR
DIRECCIÓN: UBICADO A 200M AL NORTE DE LA PLAYA LA POCITA, ALTURA DEL KM 303+200 MARGEN IZQUIERDA, EN DIRECCIÓN SUR A NORTE, DE LA CARRETERA PANAMERICANA NORTE.	PLANO N.°: 1673-2025/SBN-DGPE-SDDI M.D. N.°: 0764-2025/SBN-DGPE-SDDI		HOJA: 21-g / ESCALA: 1/750
SUBDIRECTOR: ABOG. CARLOS REATEGUIZ SANCHEZ	ELABORADO POR: BRUNO JAHIRO PINTADO CAPARACHIN	FECHA: 27/05/2025	LÁMINA: L - 01