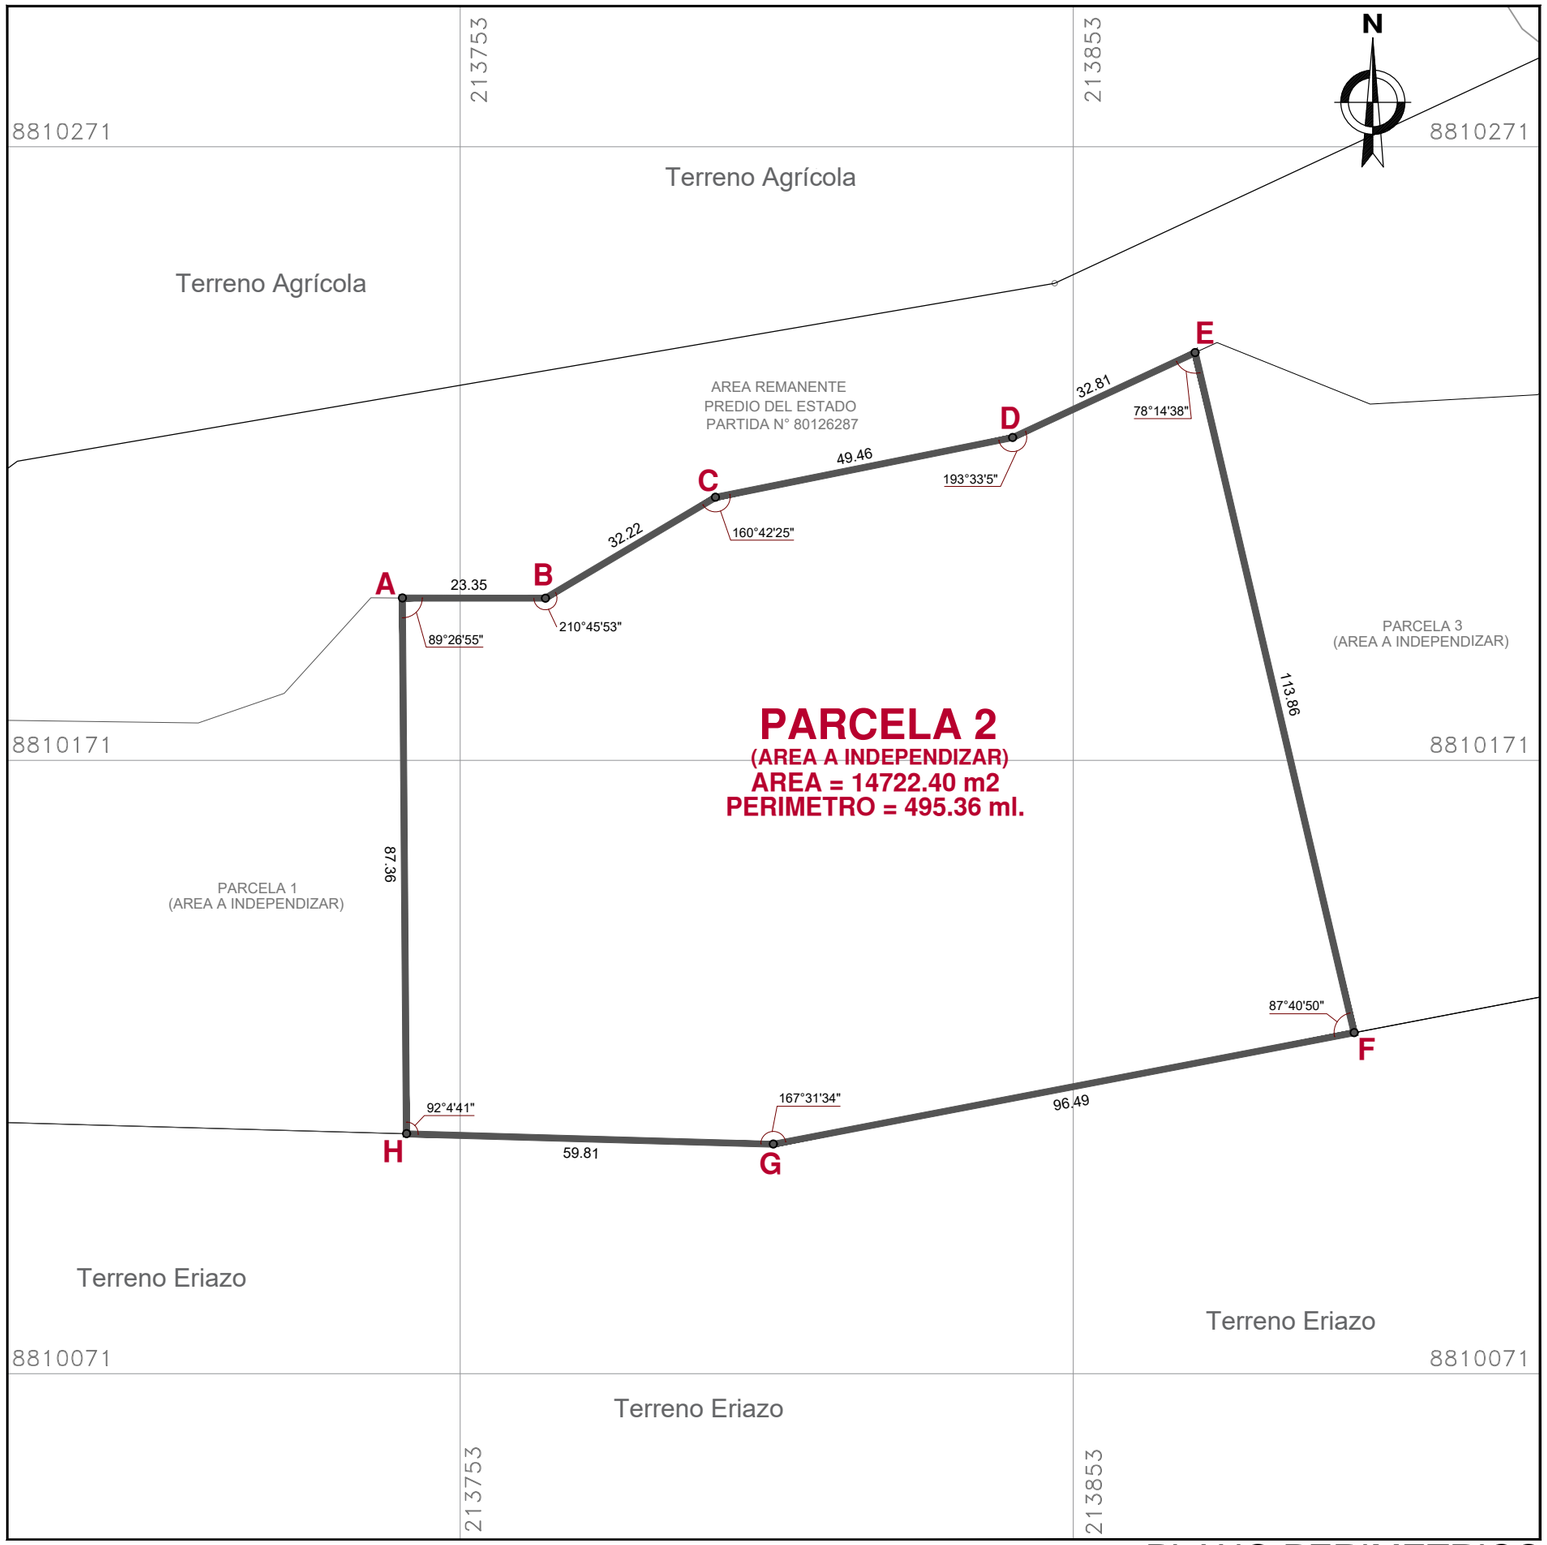



PLANO PERIMETRICO

ESCALA 1 / 1000

FUENTE : BASE GRÁFICA DE LA SBN

DISTRITO: SUPE
DATUM: PSAD 56
ZONA: 18-SUR
PROYECCIÓN: UTM

Esta es una copia auténtica imprimible de documento electrónico archivado en la Superintendencia Nacional de Bienes Estatales, aplicando lo dispuesto por el Art. 25 de DS.070-2013-PCM y la Tercera Disposición Complementaria Final del DS. 026-2016-PCM. Su autenticidad e integridad puede ser contrastada a través de la siguiente dirección web: https://app.sbn.gob.pe/verifica e ingresando la siguiente clave: 00W0682592

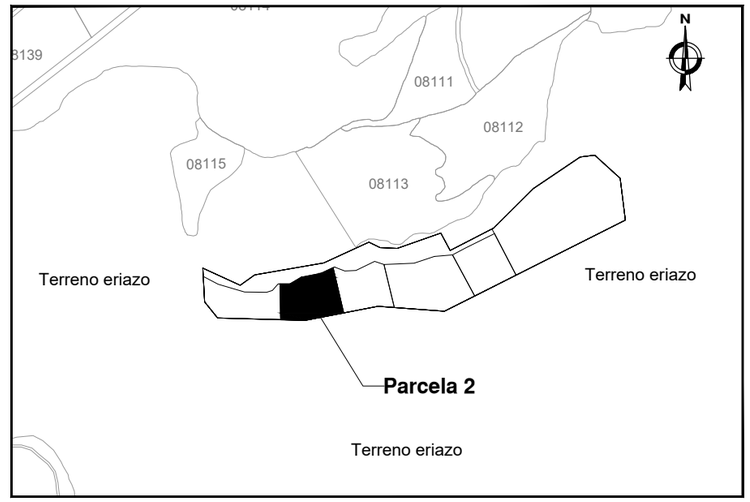

PLANO DE UBICACIÓN

ESCALA 1/15 000

CUADRO DE DATOS TÉCNICOS				ZONA: 18S, SISTEMA COORDENADA UTM DATUM PSAD 56		ZONA: 18S, SISTEMA COORDENADA UTM DATUM WGS 84	
VERTICE	LADO	DISTANCIA	ANG. INTERNO	ESTE (X)	NORTE (Y)	ESTE (X)	NORTE (Y)
A	A–B	23.35	89°26'55"	213743.5501	8810197.4557	213523.0925	8809826.7854
B	B–C	32.22	210°45'53"	213766.8988	8810197.4174	213546.4412	8809826.7471
C	C–D	49.46	160°42'25"	213794.6119	8810213.8530	213574.1543	8809843.1827
D	D–E	32.81	193°33'5"	213843.0977	8810223.6095	213622.6401	8809852.9392
E	E–F	113.86	78°14'38"	213872.8515	8810237.4389	213652.3939	8809866.7686
F	F–G	96.49	87°40'50"	213898.7981	8810126.5755	213678.3405	8809755.9052
G	G–H	59.81	167°31'34"	213804.0329	8810108.4073	213583.5753	8809737.7370
H	H–A	87.36	92°4'41"	213744.2473	8810110.0991	213523.7897	8809739.4288
TOTAL		495.36	1080°0'1"				

Firmado digitalmente por:
CHILCCE CRUZ Jaime Epifanio FAU
20131057823 hard
Fecha: 24/04/2025 09:36:49-0500

ING. JAIME CHILCCE CRUZ
INGENIERO GEÓGRAFO
CIP N° 66826

Fuente: Base Gráfica SBN, llevada a Datum WGS 84 con software QGIS V. 2.18 solo para fines referenciales

SUPERINTENDENCIA NACIONAL DE BIENES ESTATALES
SUBDIRECCIÓN DE DESARROLLO INMOBILIARIO

PLANO: PERIMÉTRICO Y UBICACIÓN		**EXPEDIENTE:** 425–2023/SBNSDDI **CUS MATRIZ N°:** 95099
DENOMINACIÓN: PARCELA 2 (area a independizar)	**DISTRITO:** SUPE **PROVINCIA:** BARRANCA **DPTO:** LIMA	**ÁREA:** 14 722.40 m² **ZONA:** 18 SUR
DIRECCIÓN: Se ubica al pie del Cerro Purmacana, a la altura del Centro Poblado Virgen del Rosario, girando en dirección sur por una trocha carrozable hasta llegar al predio	**PLANO N°:** 1108-2025/SBNSDDI **M.D. N°:** 0501-2025/SBN-DGPE-SDDI	**ESCALAS:** INDICADAS **VERSIÓN:** 01
SUBDIRECTOR: ABG. CARLOS RETAEGUI SANCHEZ	**ELABORADO POR:** PIERO GÓMEZ RAMÍREZ	**FECHA:** 24/04/2025 **LÁMINA:** L - 01